

花藝設計師工作室


學號：51237128 姓名：廖和風
指導老師：陳敬良

設計說明：


用不同大小的方塊區分空間，再利用二樓建築物角落的尖角、圓角穿插，製造更多焦點目光，凸顯建築物。

將私人空間與工作空間設置在一樓，公共空間設置在二樓(泡湯空間除外)，區分空間用途。


泡湯空間利用視角的角度差，讓外面看不到裡面，但使用者會感受像在半室外。

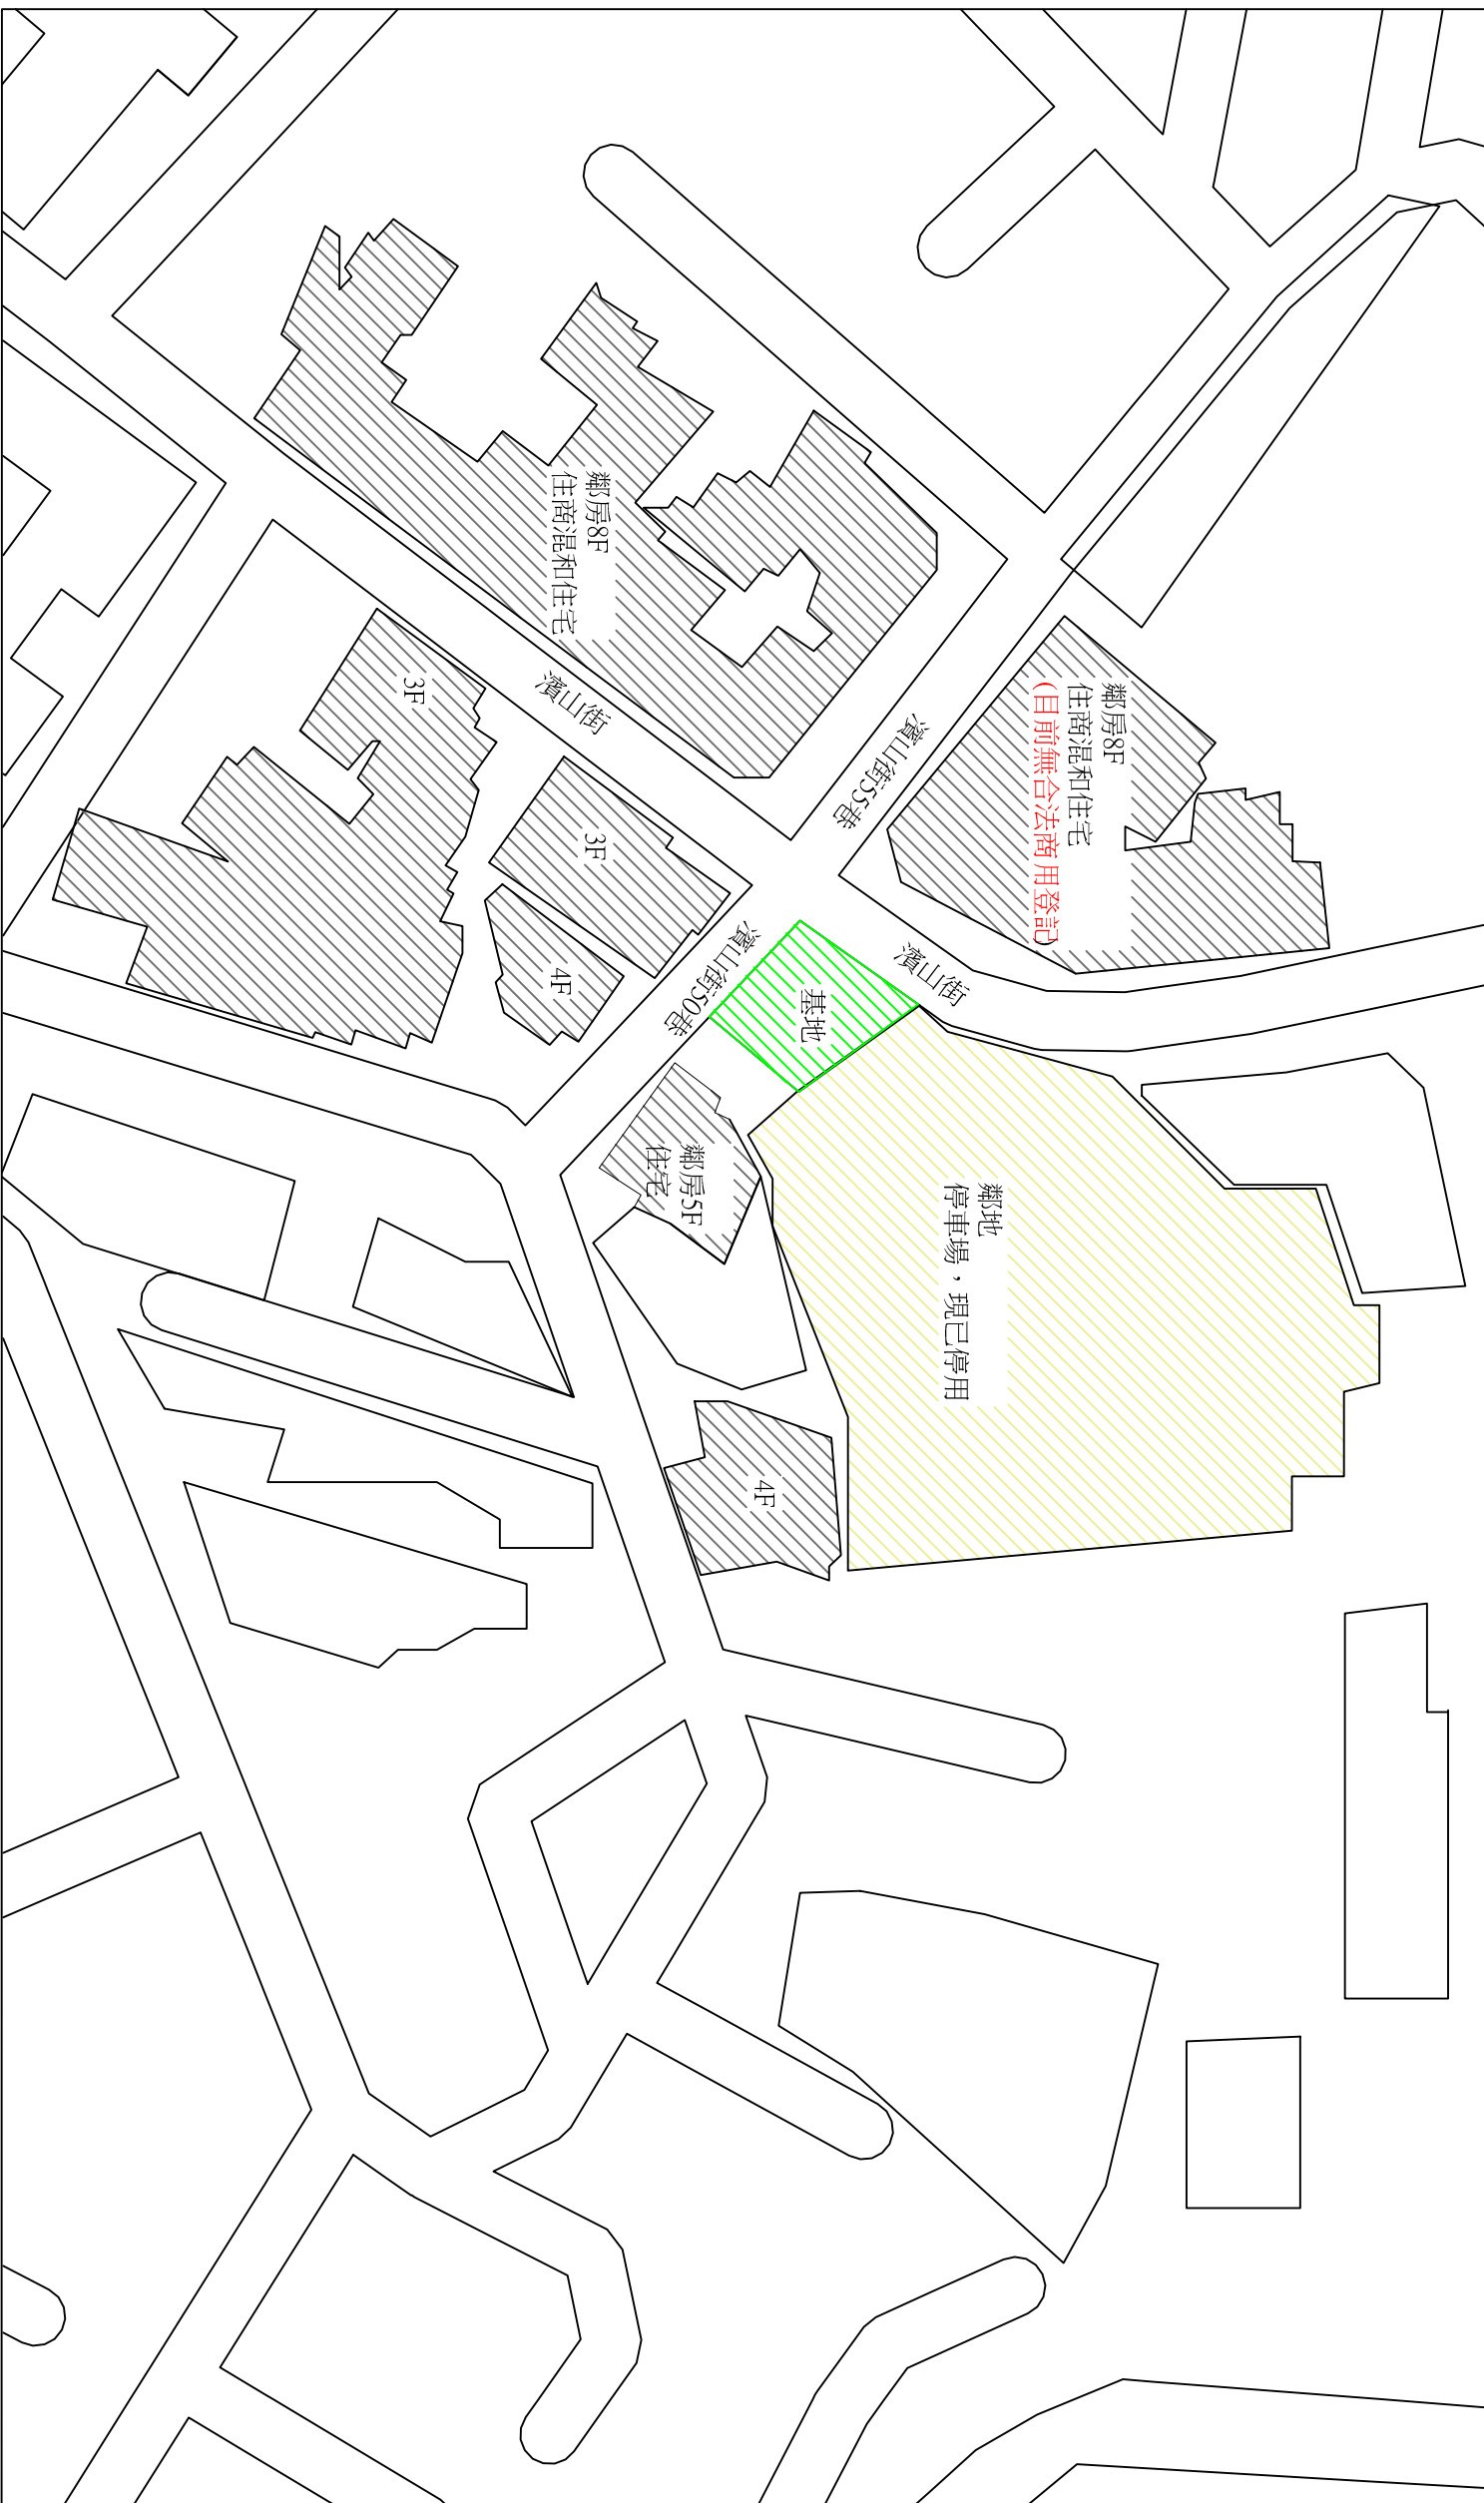

基地配置圖 比例：1/1000

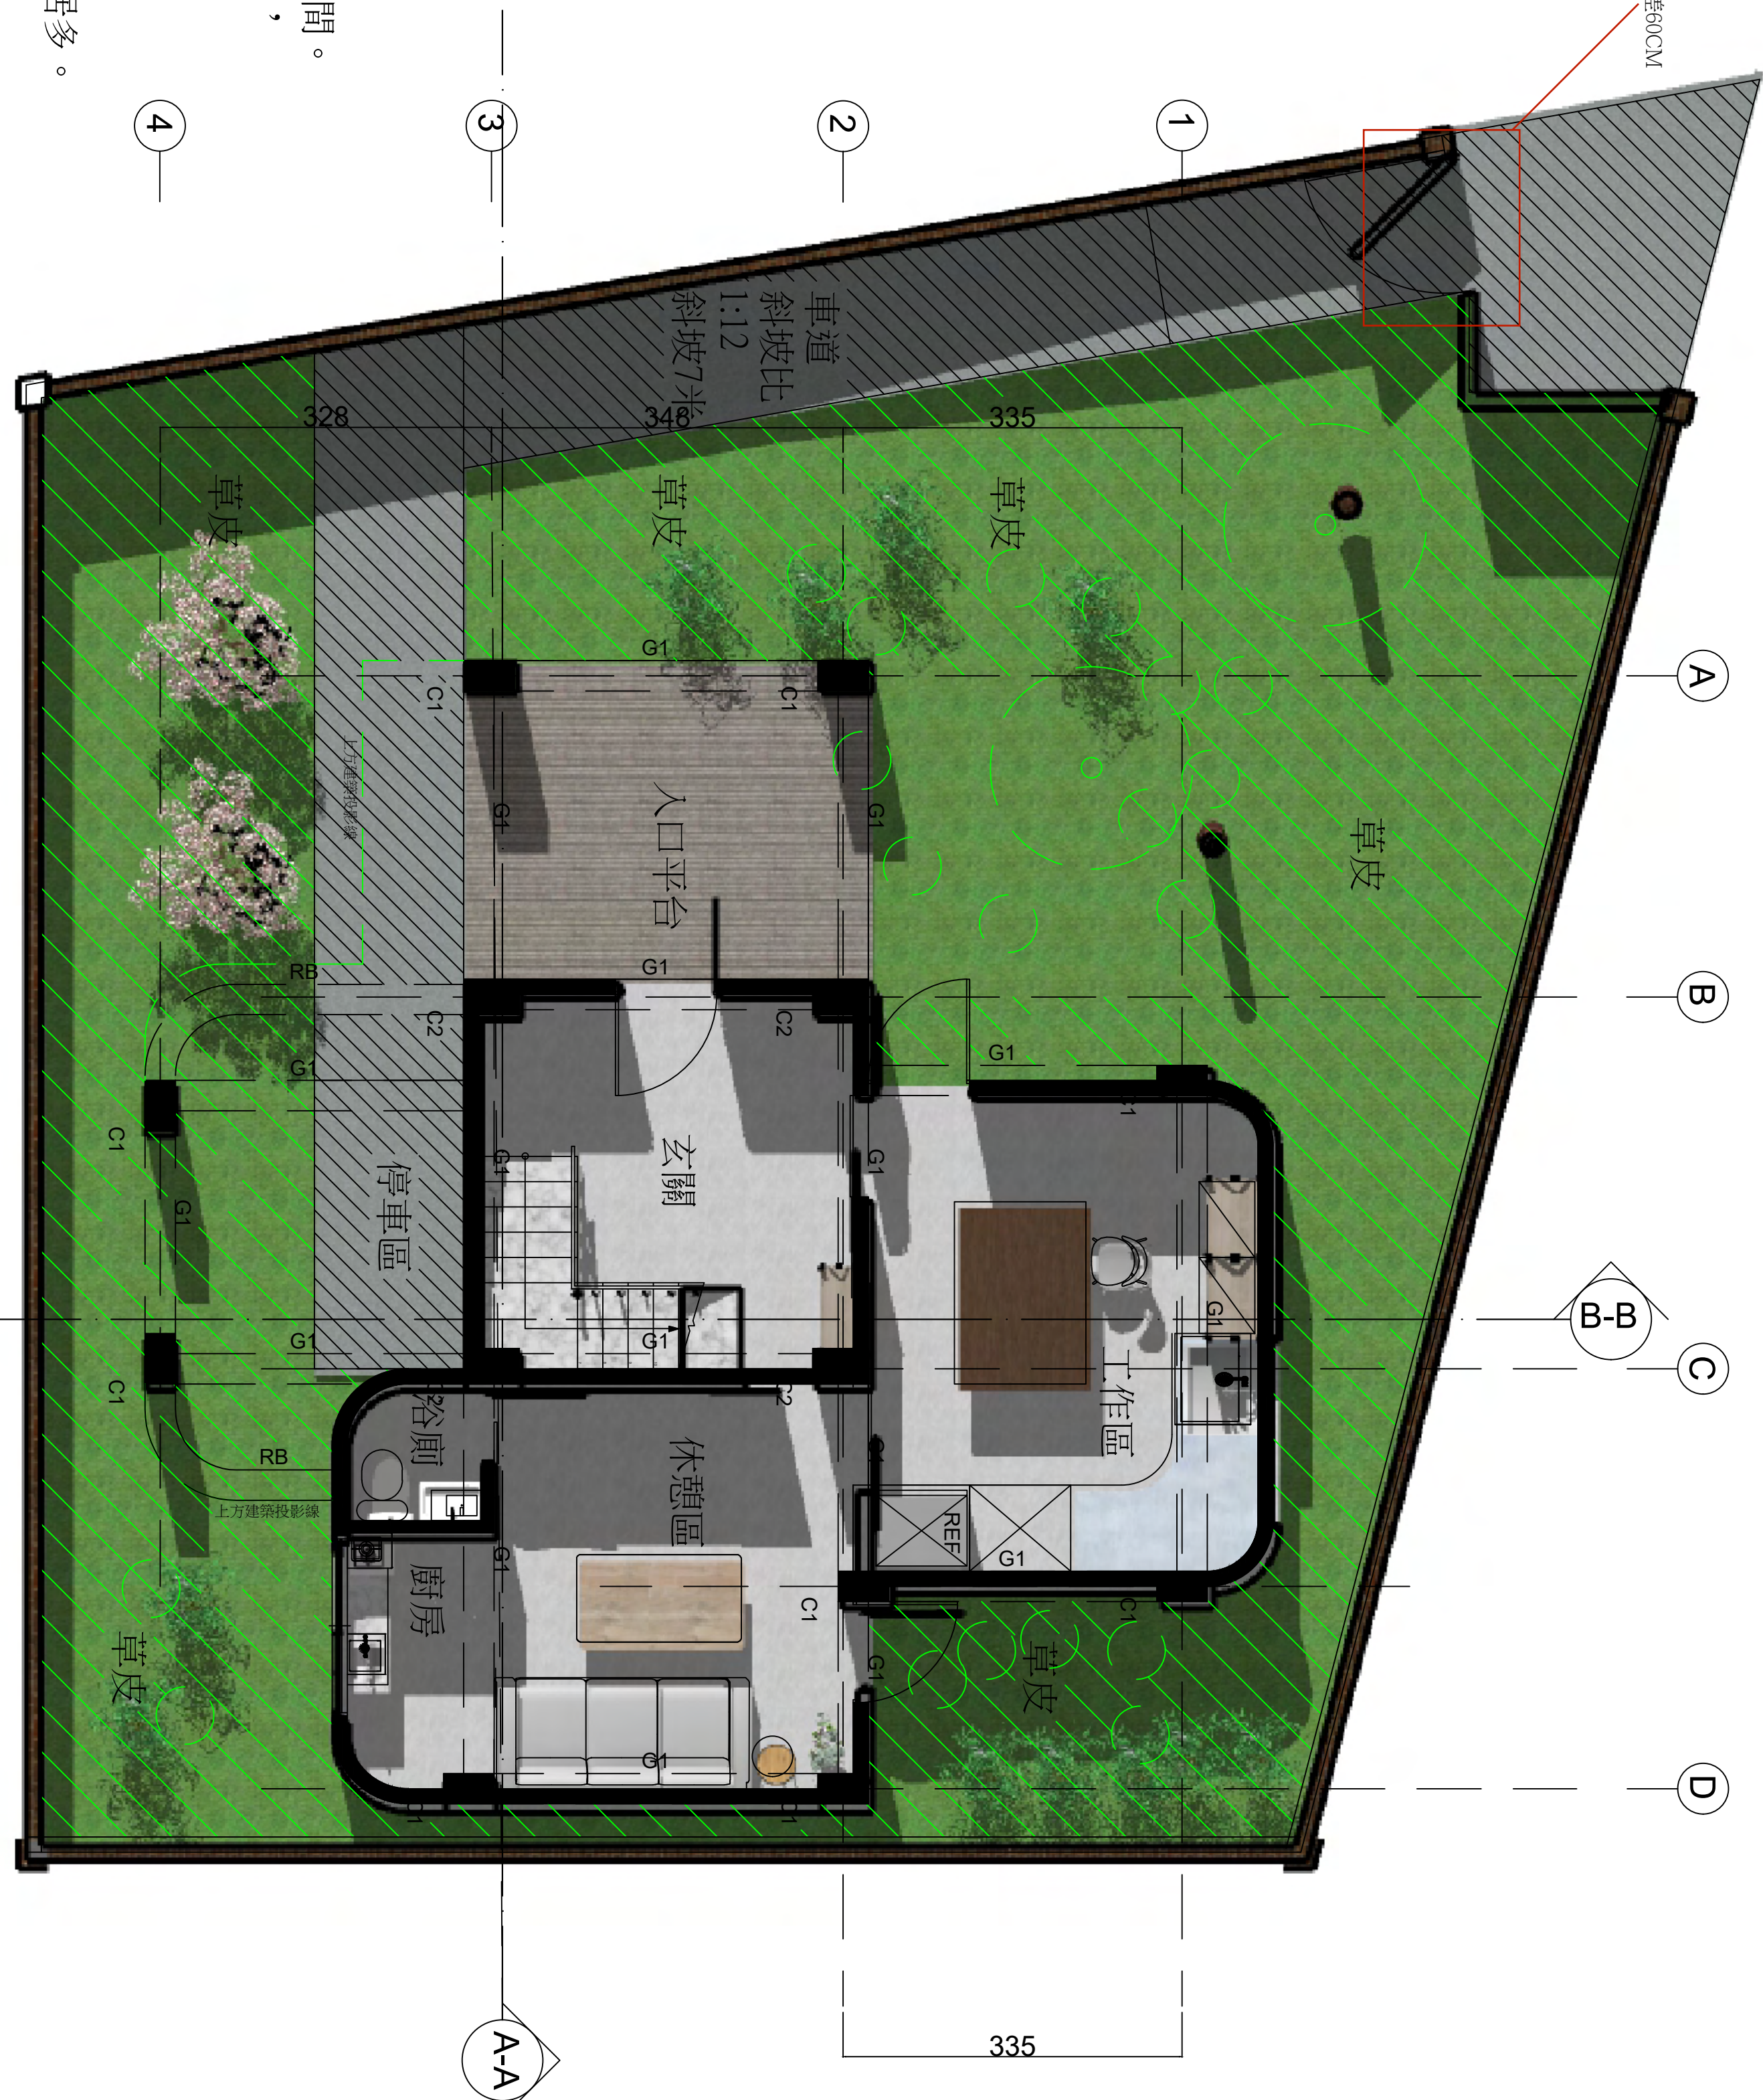

一層平面圖比例：1/50

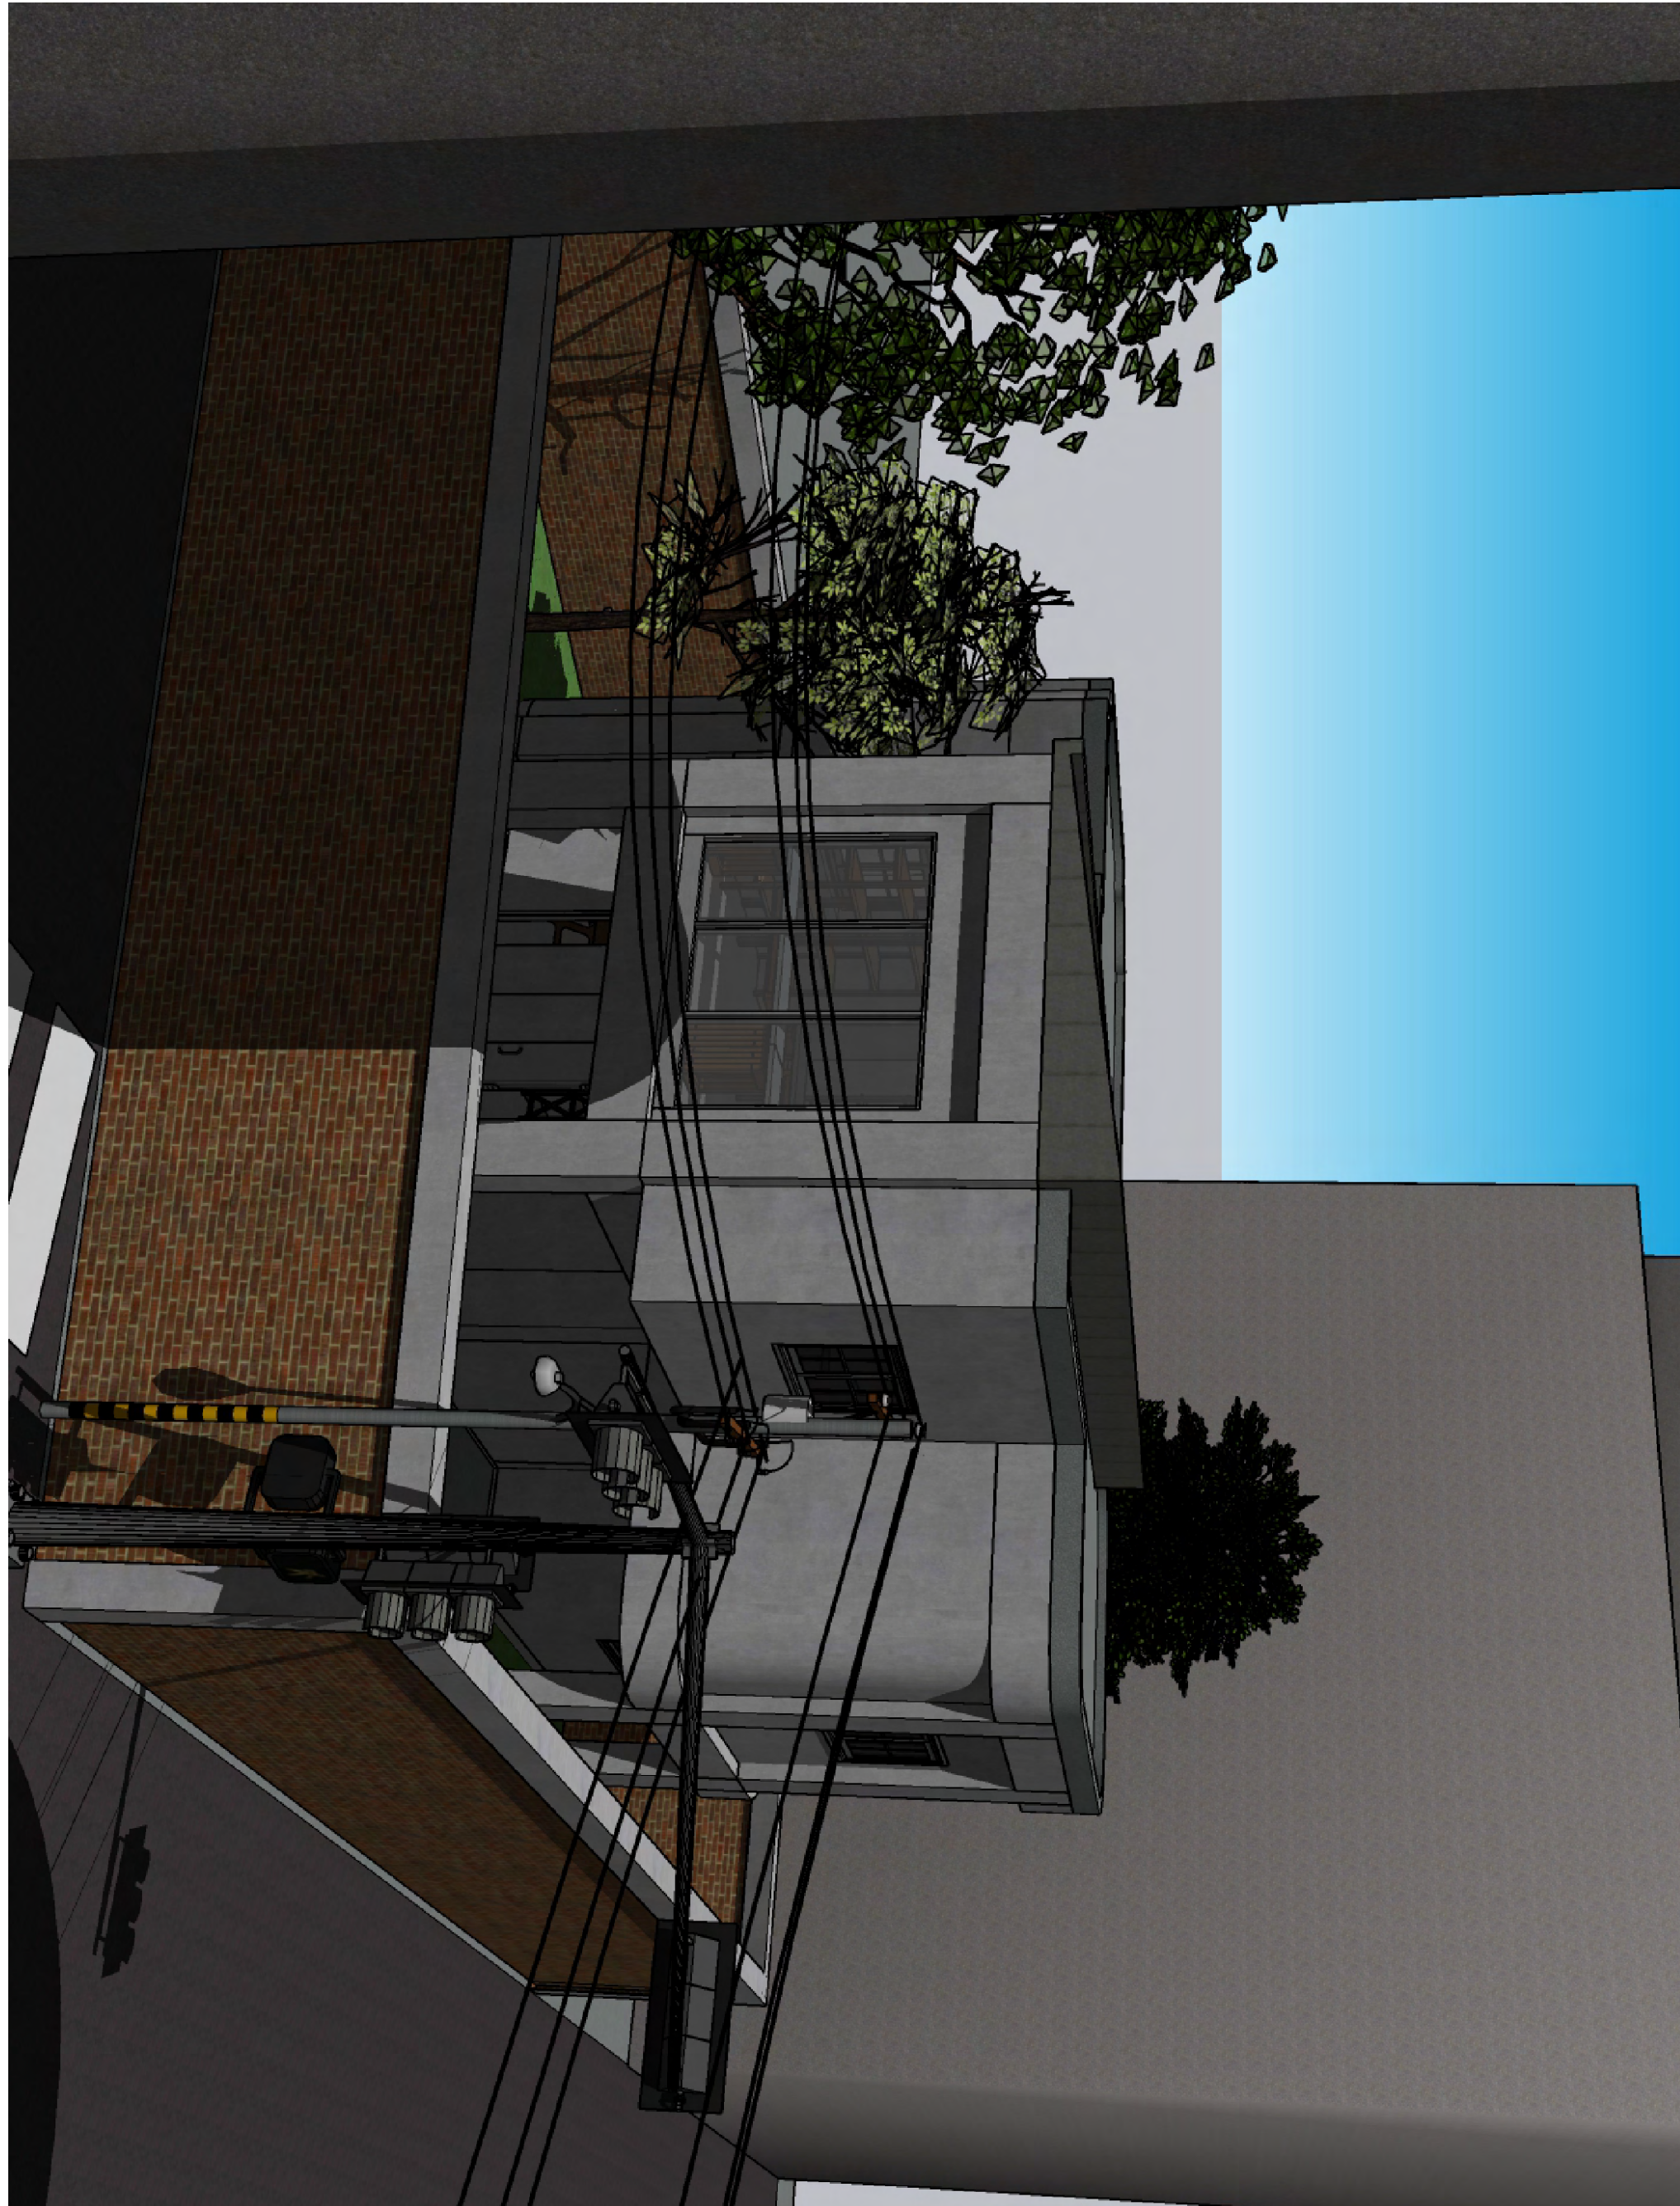


透視圖-行人視角




透視圖




- 人潮分析
- 學生和老師 (正修、文山高中)
 - 出現時間：通常為上、下班，午休時間。
 - 上下班時段：以機車居多，車輛其次，少許行人，有少量腳踏車。
 - 午休時間：以機車居多，行人其次。目的多為文山街的餐廳。
 - 往晨康
 - 病患 或 家屬，全天都會經過，汽車居多。
 - 專車：長庚專車 (小巴士)。
- 人車衝突 空間現況與影響
- 此路段皆無人行道，店家也都裝潢加蓋到滿。
 - 因此行人不好行走，直到旁邊的空地。
 - 交通工具主要出現數量：機車 > 汽車 > 行人 > 腳踏車 > 小巴士。
- 附近建築元素、街道與建築特徵
- 二到七層樓高，一樓有商店、飯館的建築物。
 - 對面的紅磚鋪面建築。
 - 大量店家招牌。
 - 鐵皮屋、鐵皮屋頂。
 - 學生宿舍、出租套房。
- 廢氣主要來源、污染源
- 車輛排氣。
 - 餐廳排氣。
- 噪音來源(主要源於車流)
- 人車衝突範圍
 - 日照
 - 廢氣
 - 氣流(街道形成穿堂風)
 - 其他影響因素
- 車輛路線
- 行人動線
 - 外部視線

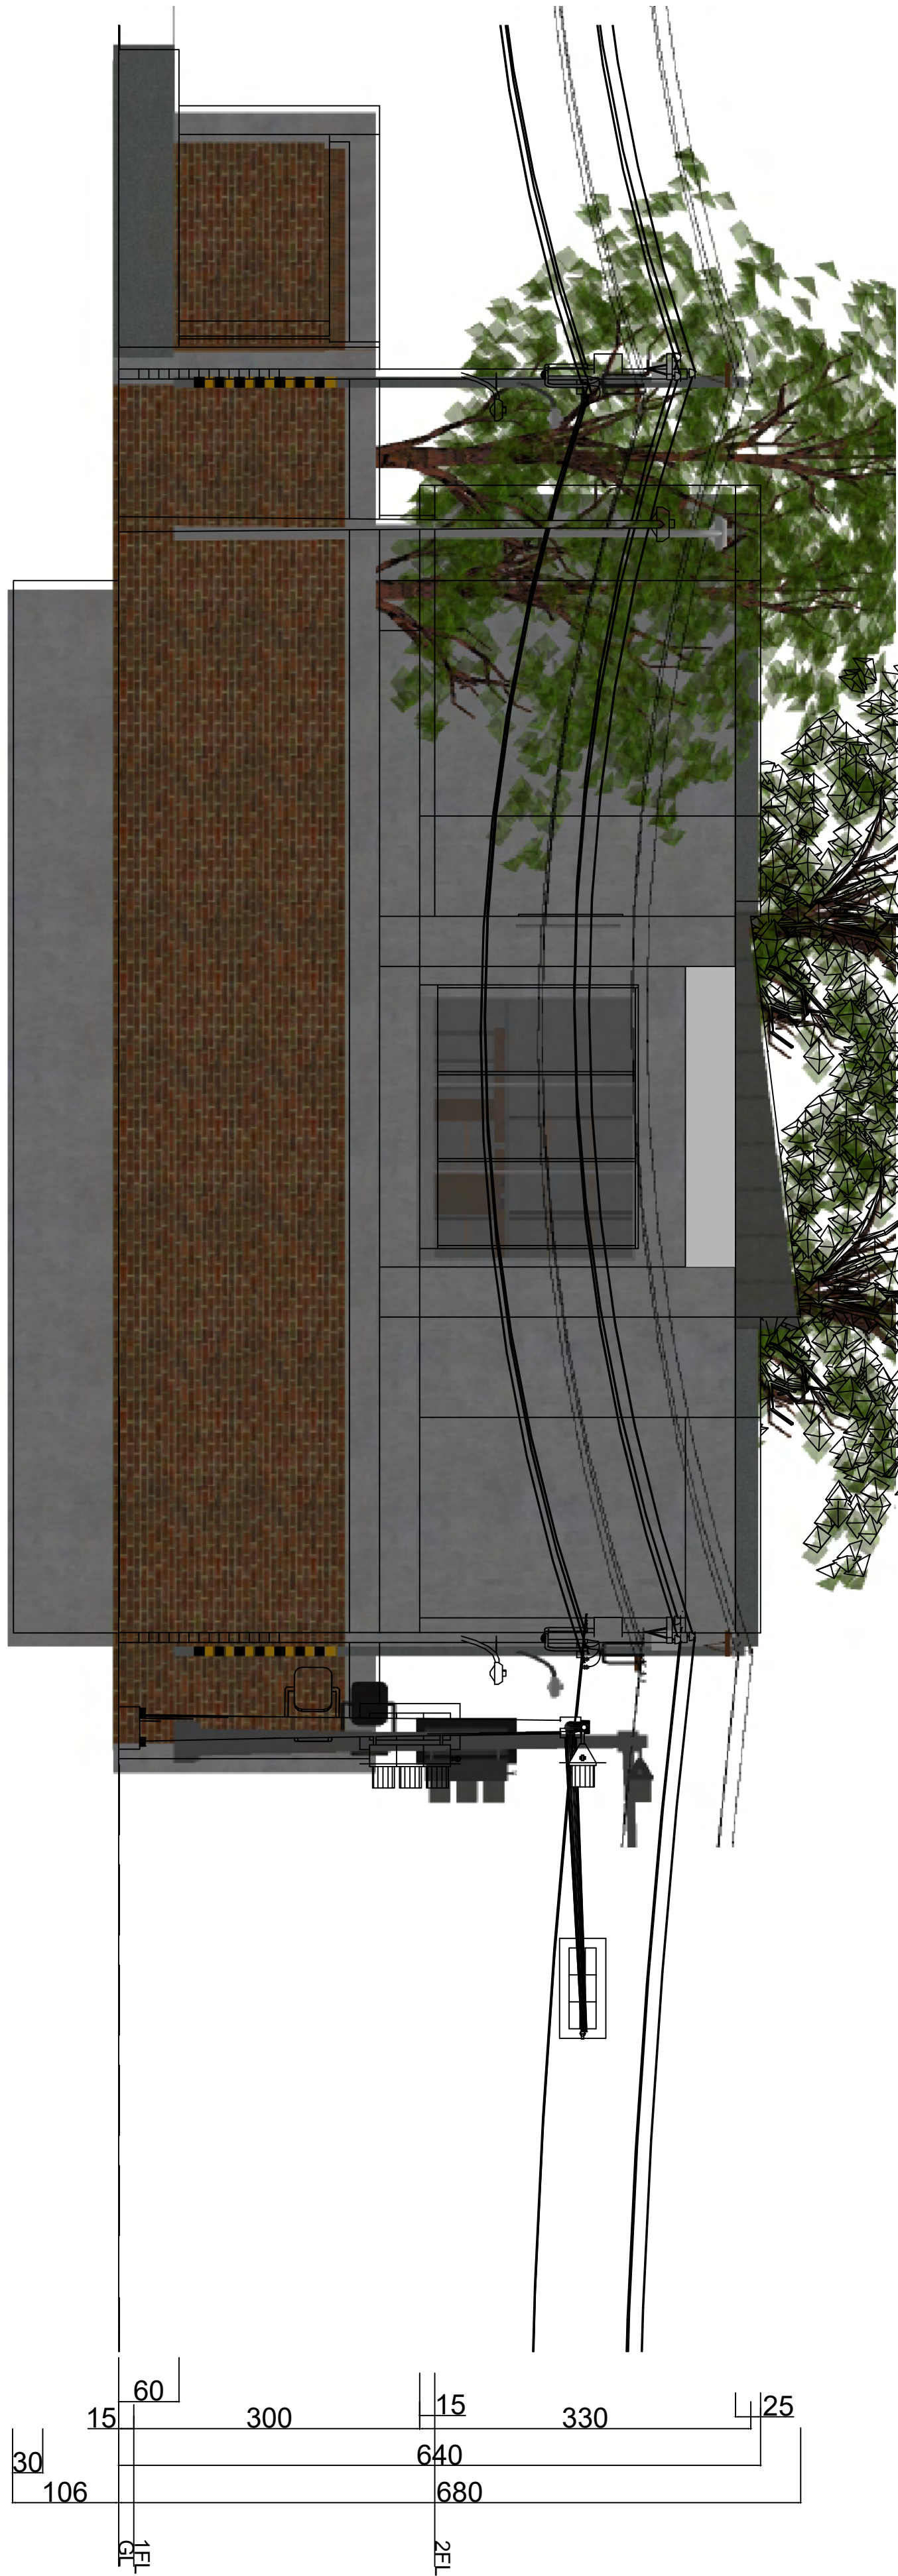


東向立面圖比例：1/50

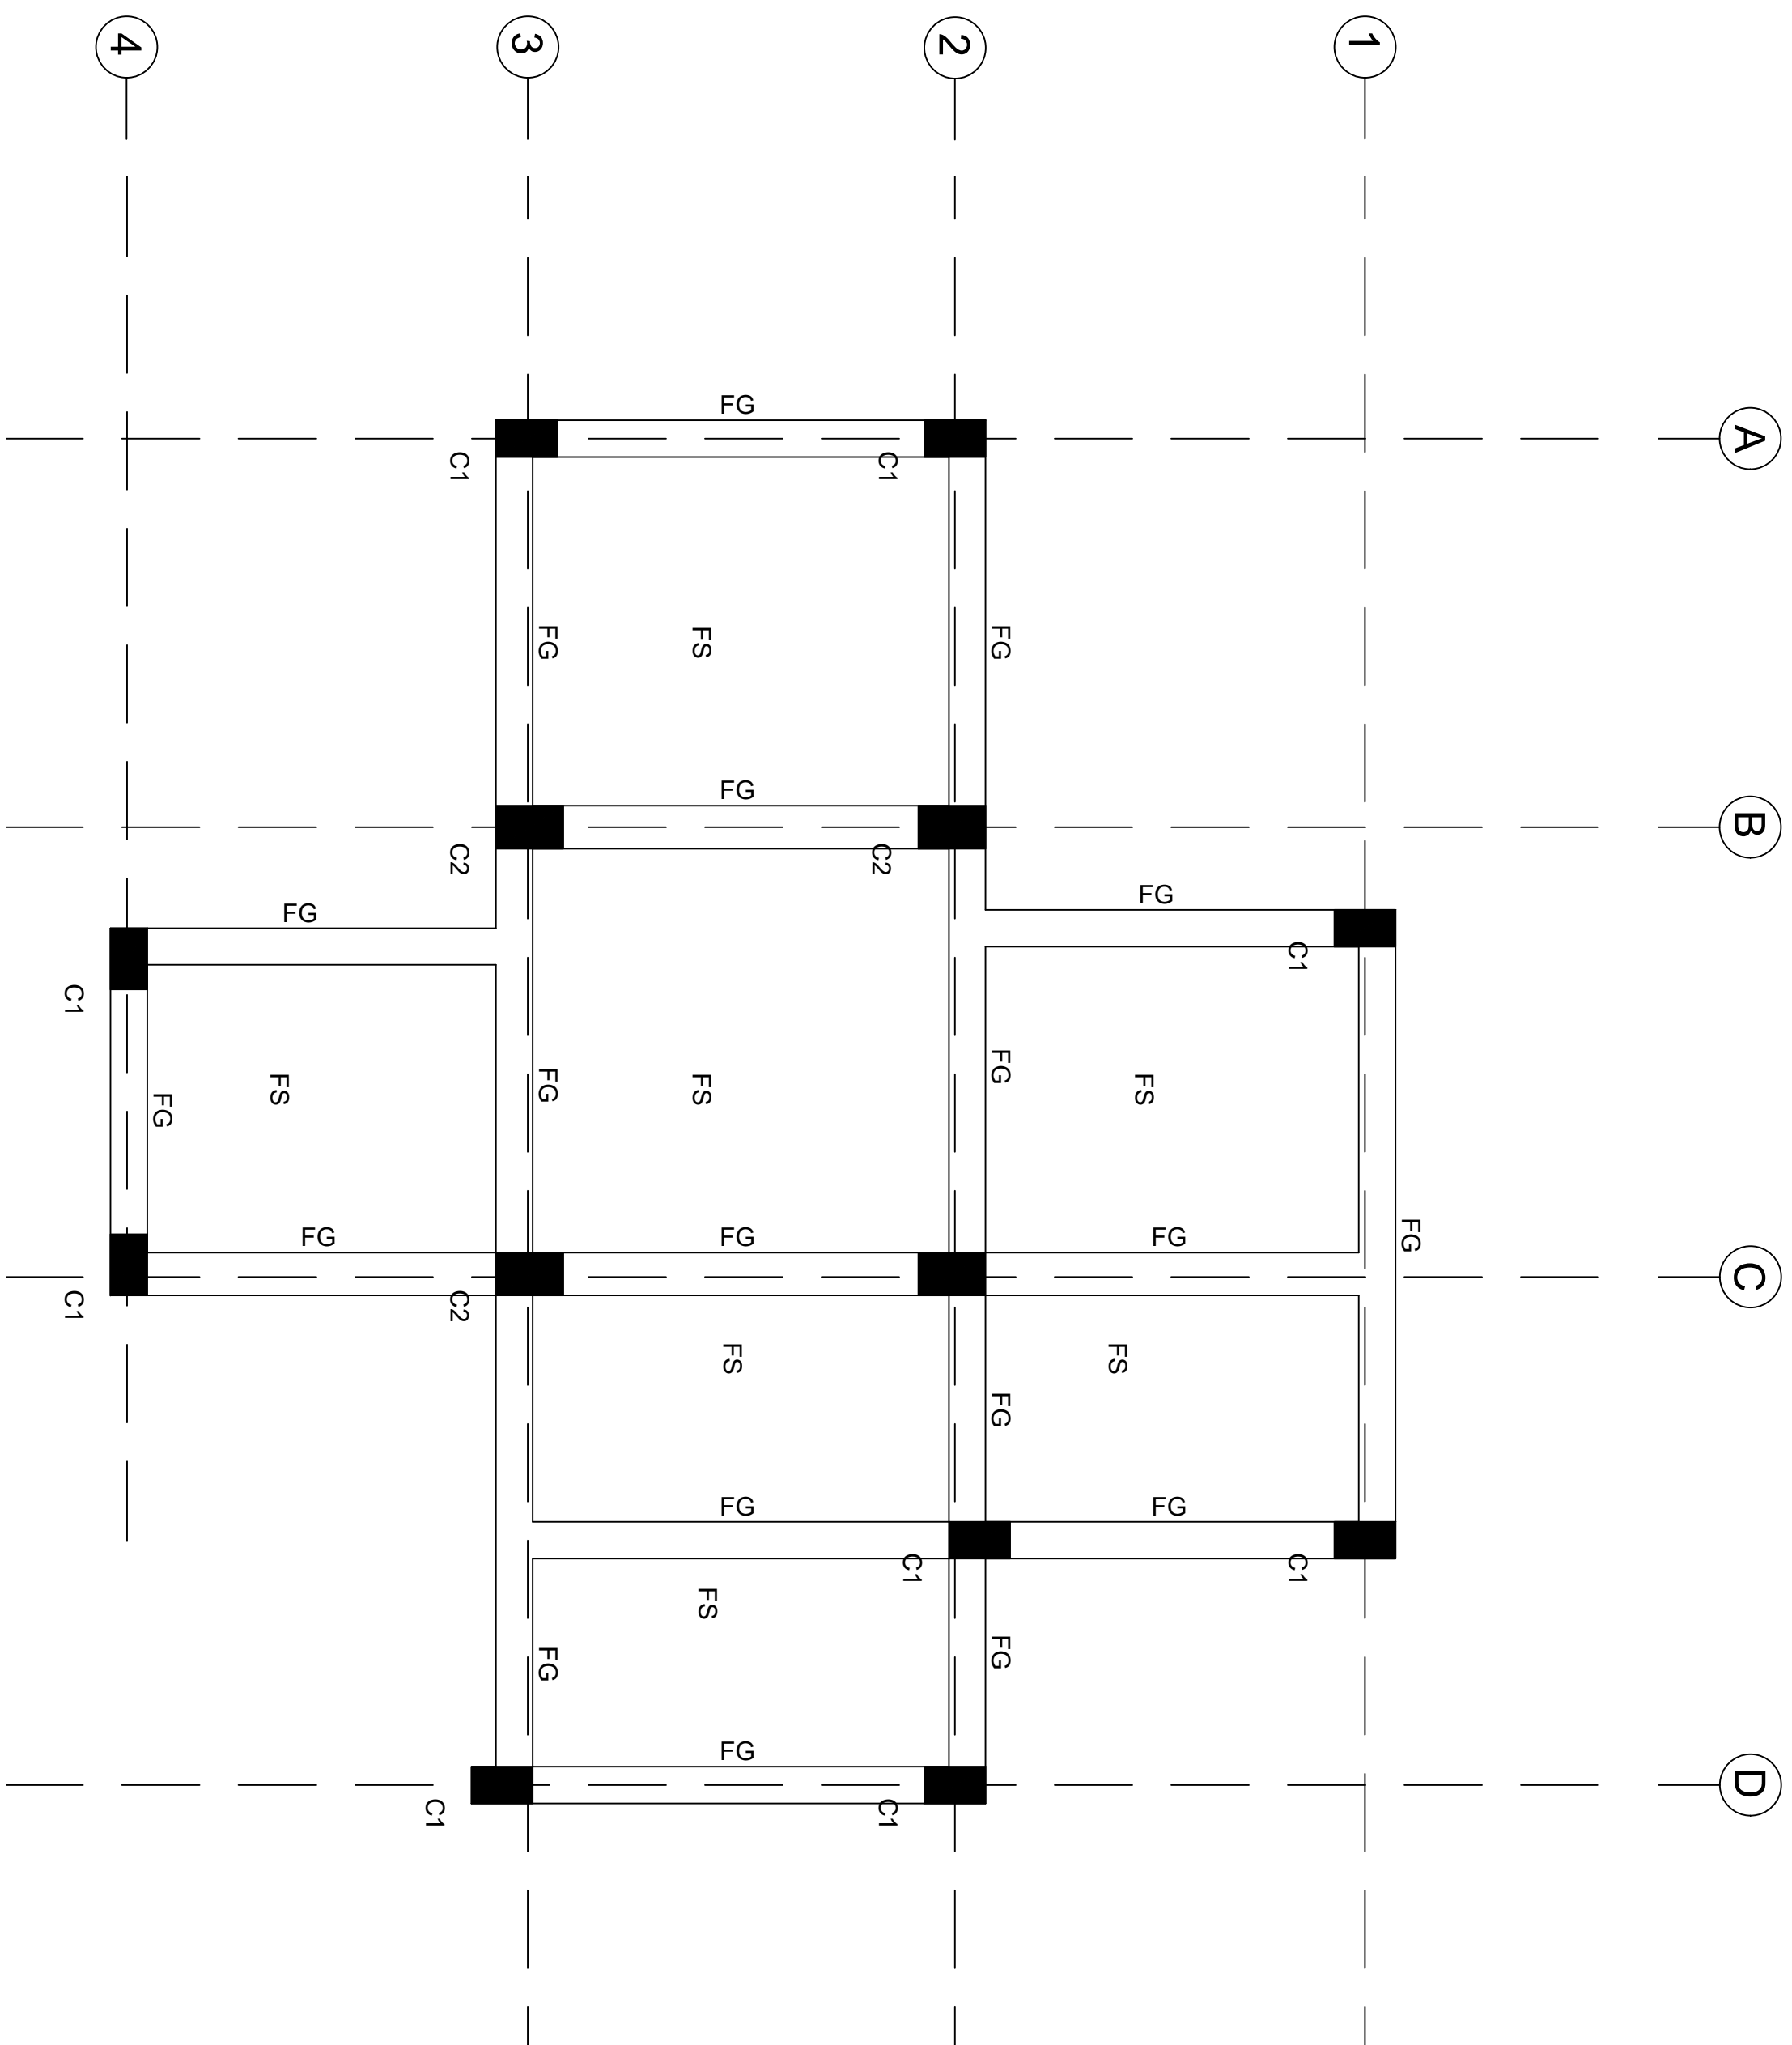

基礎平面圖 比例：1/50

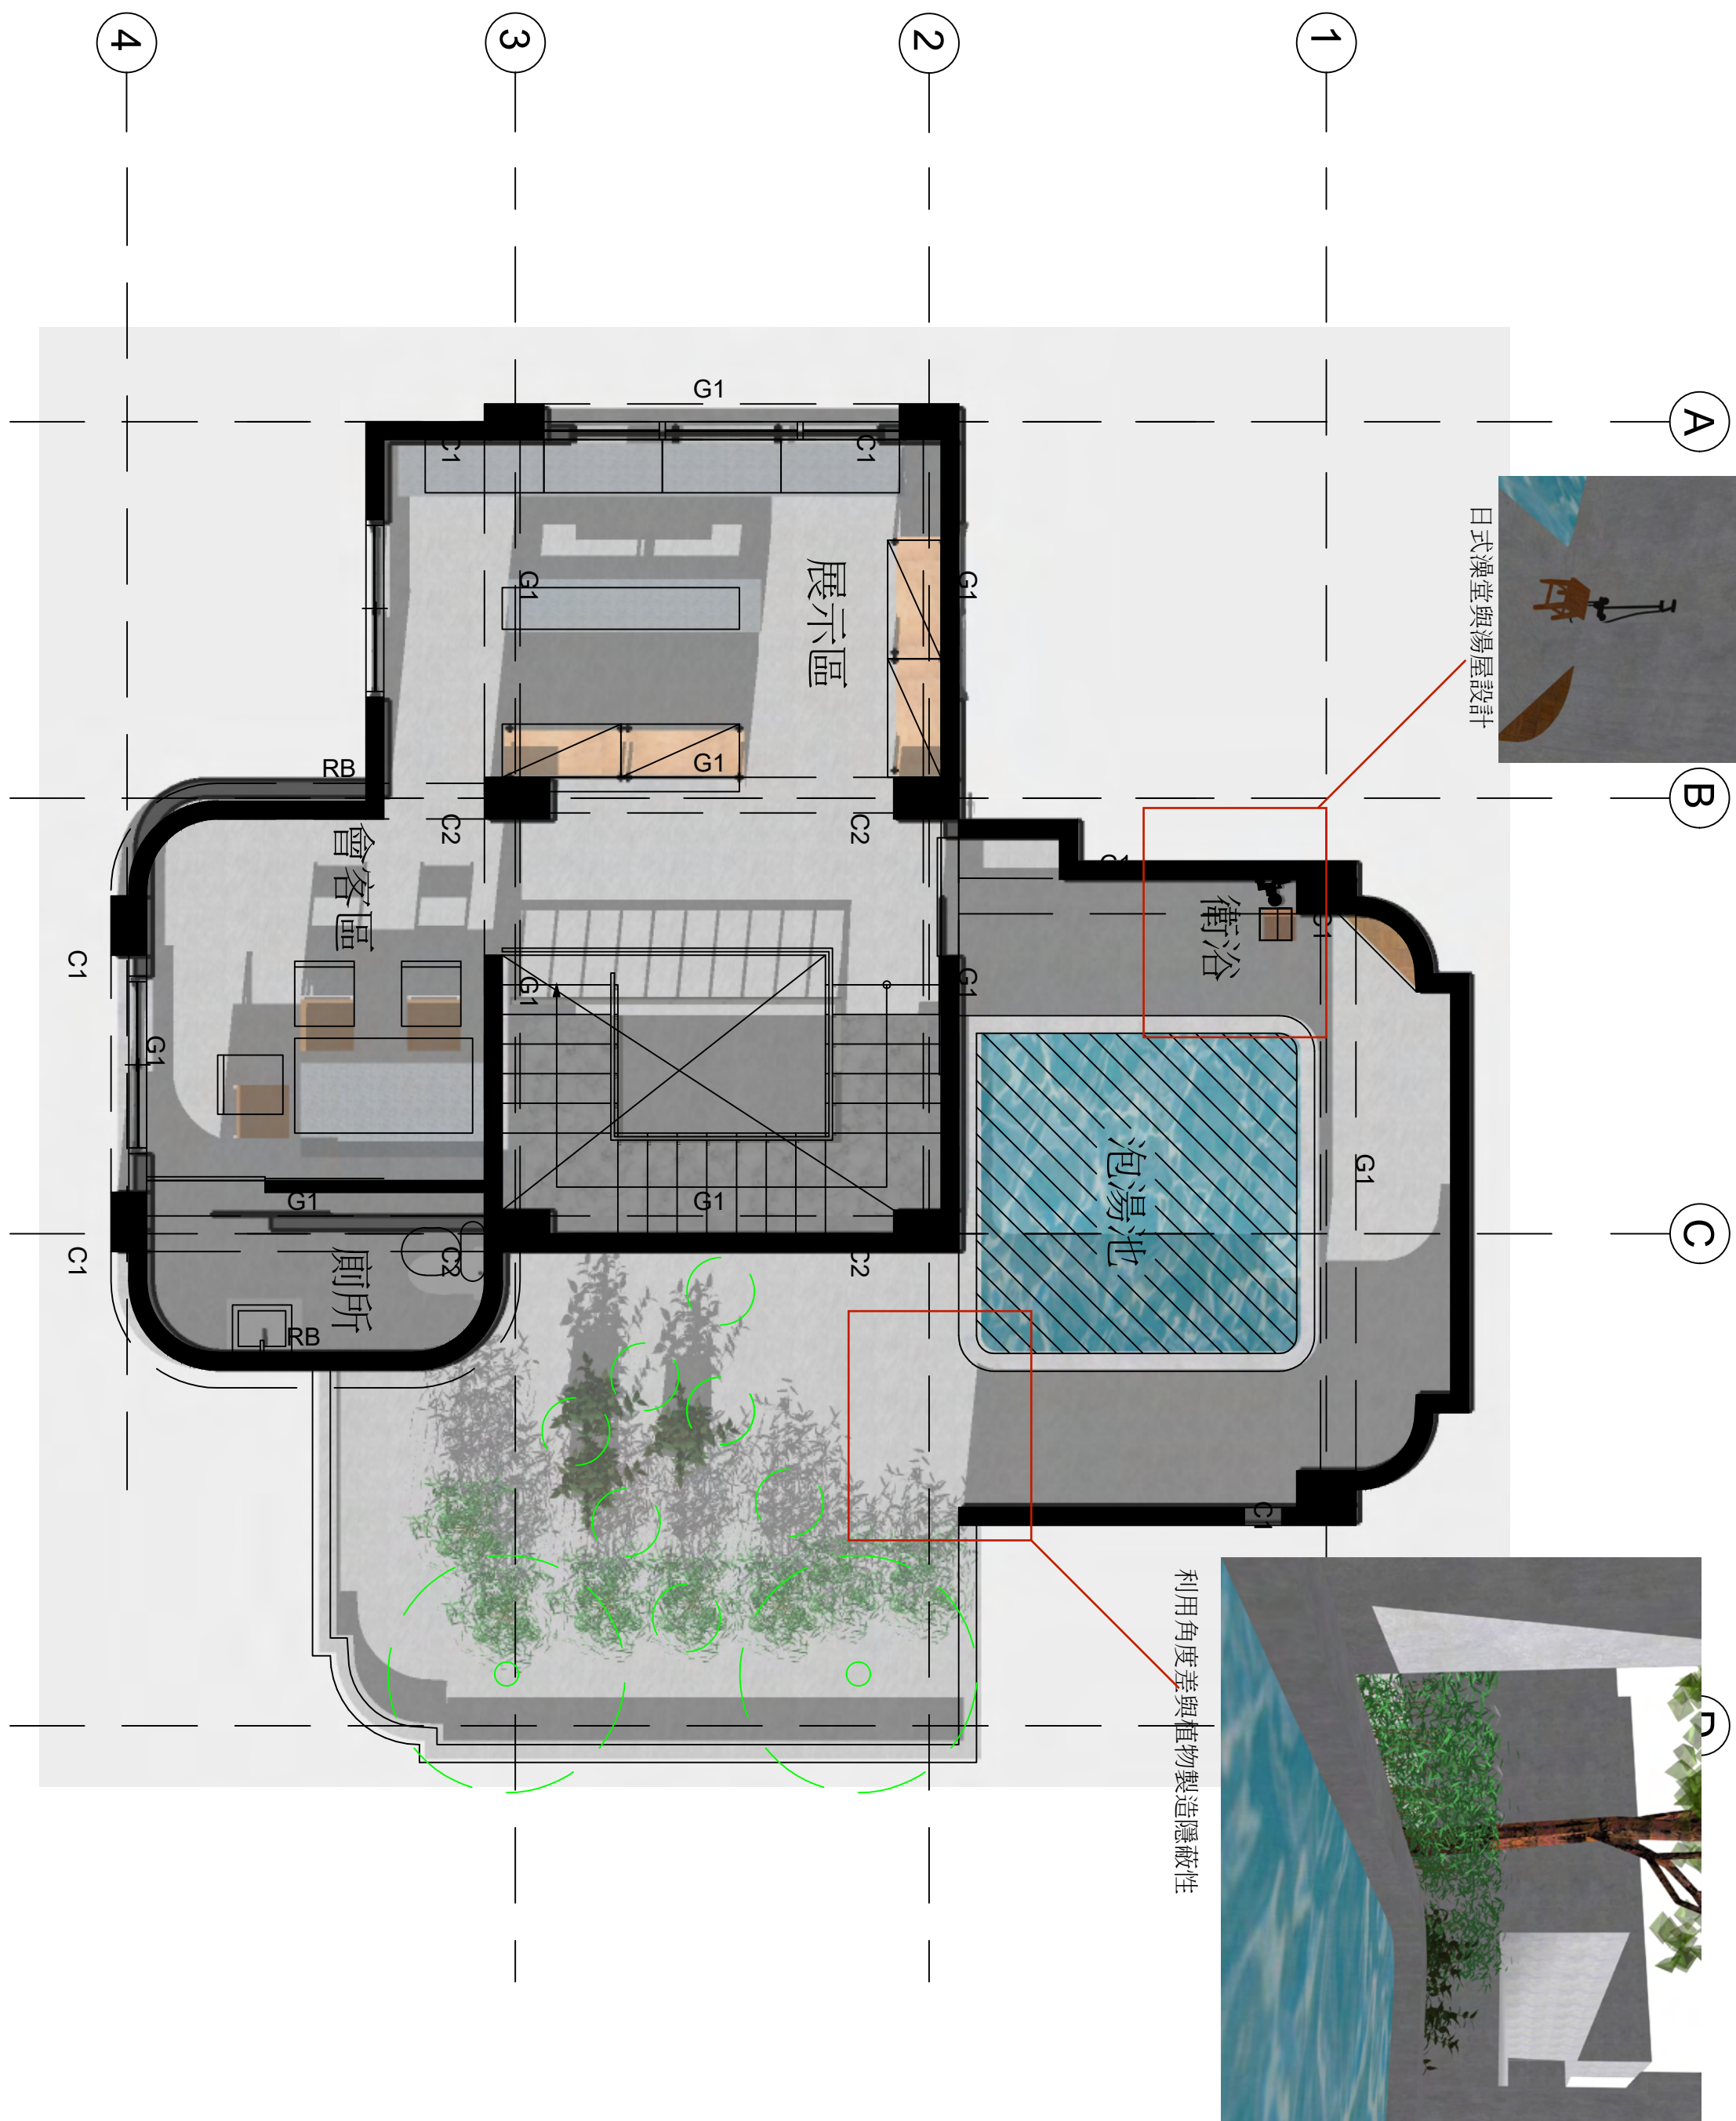

二層平面圖 比例：1/50

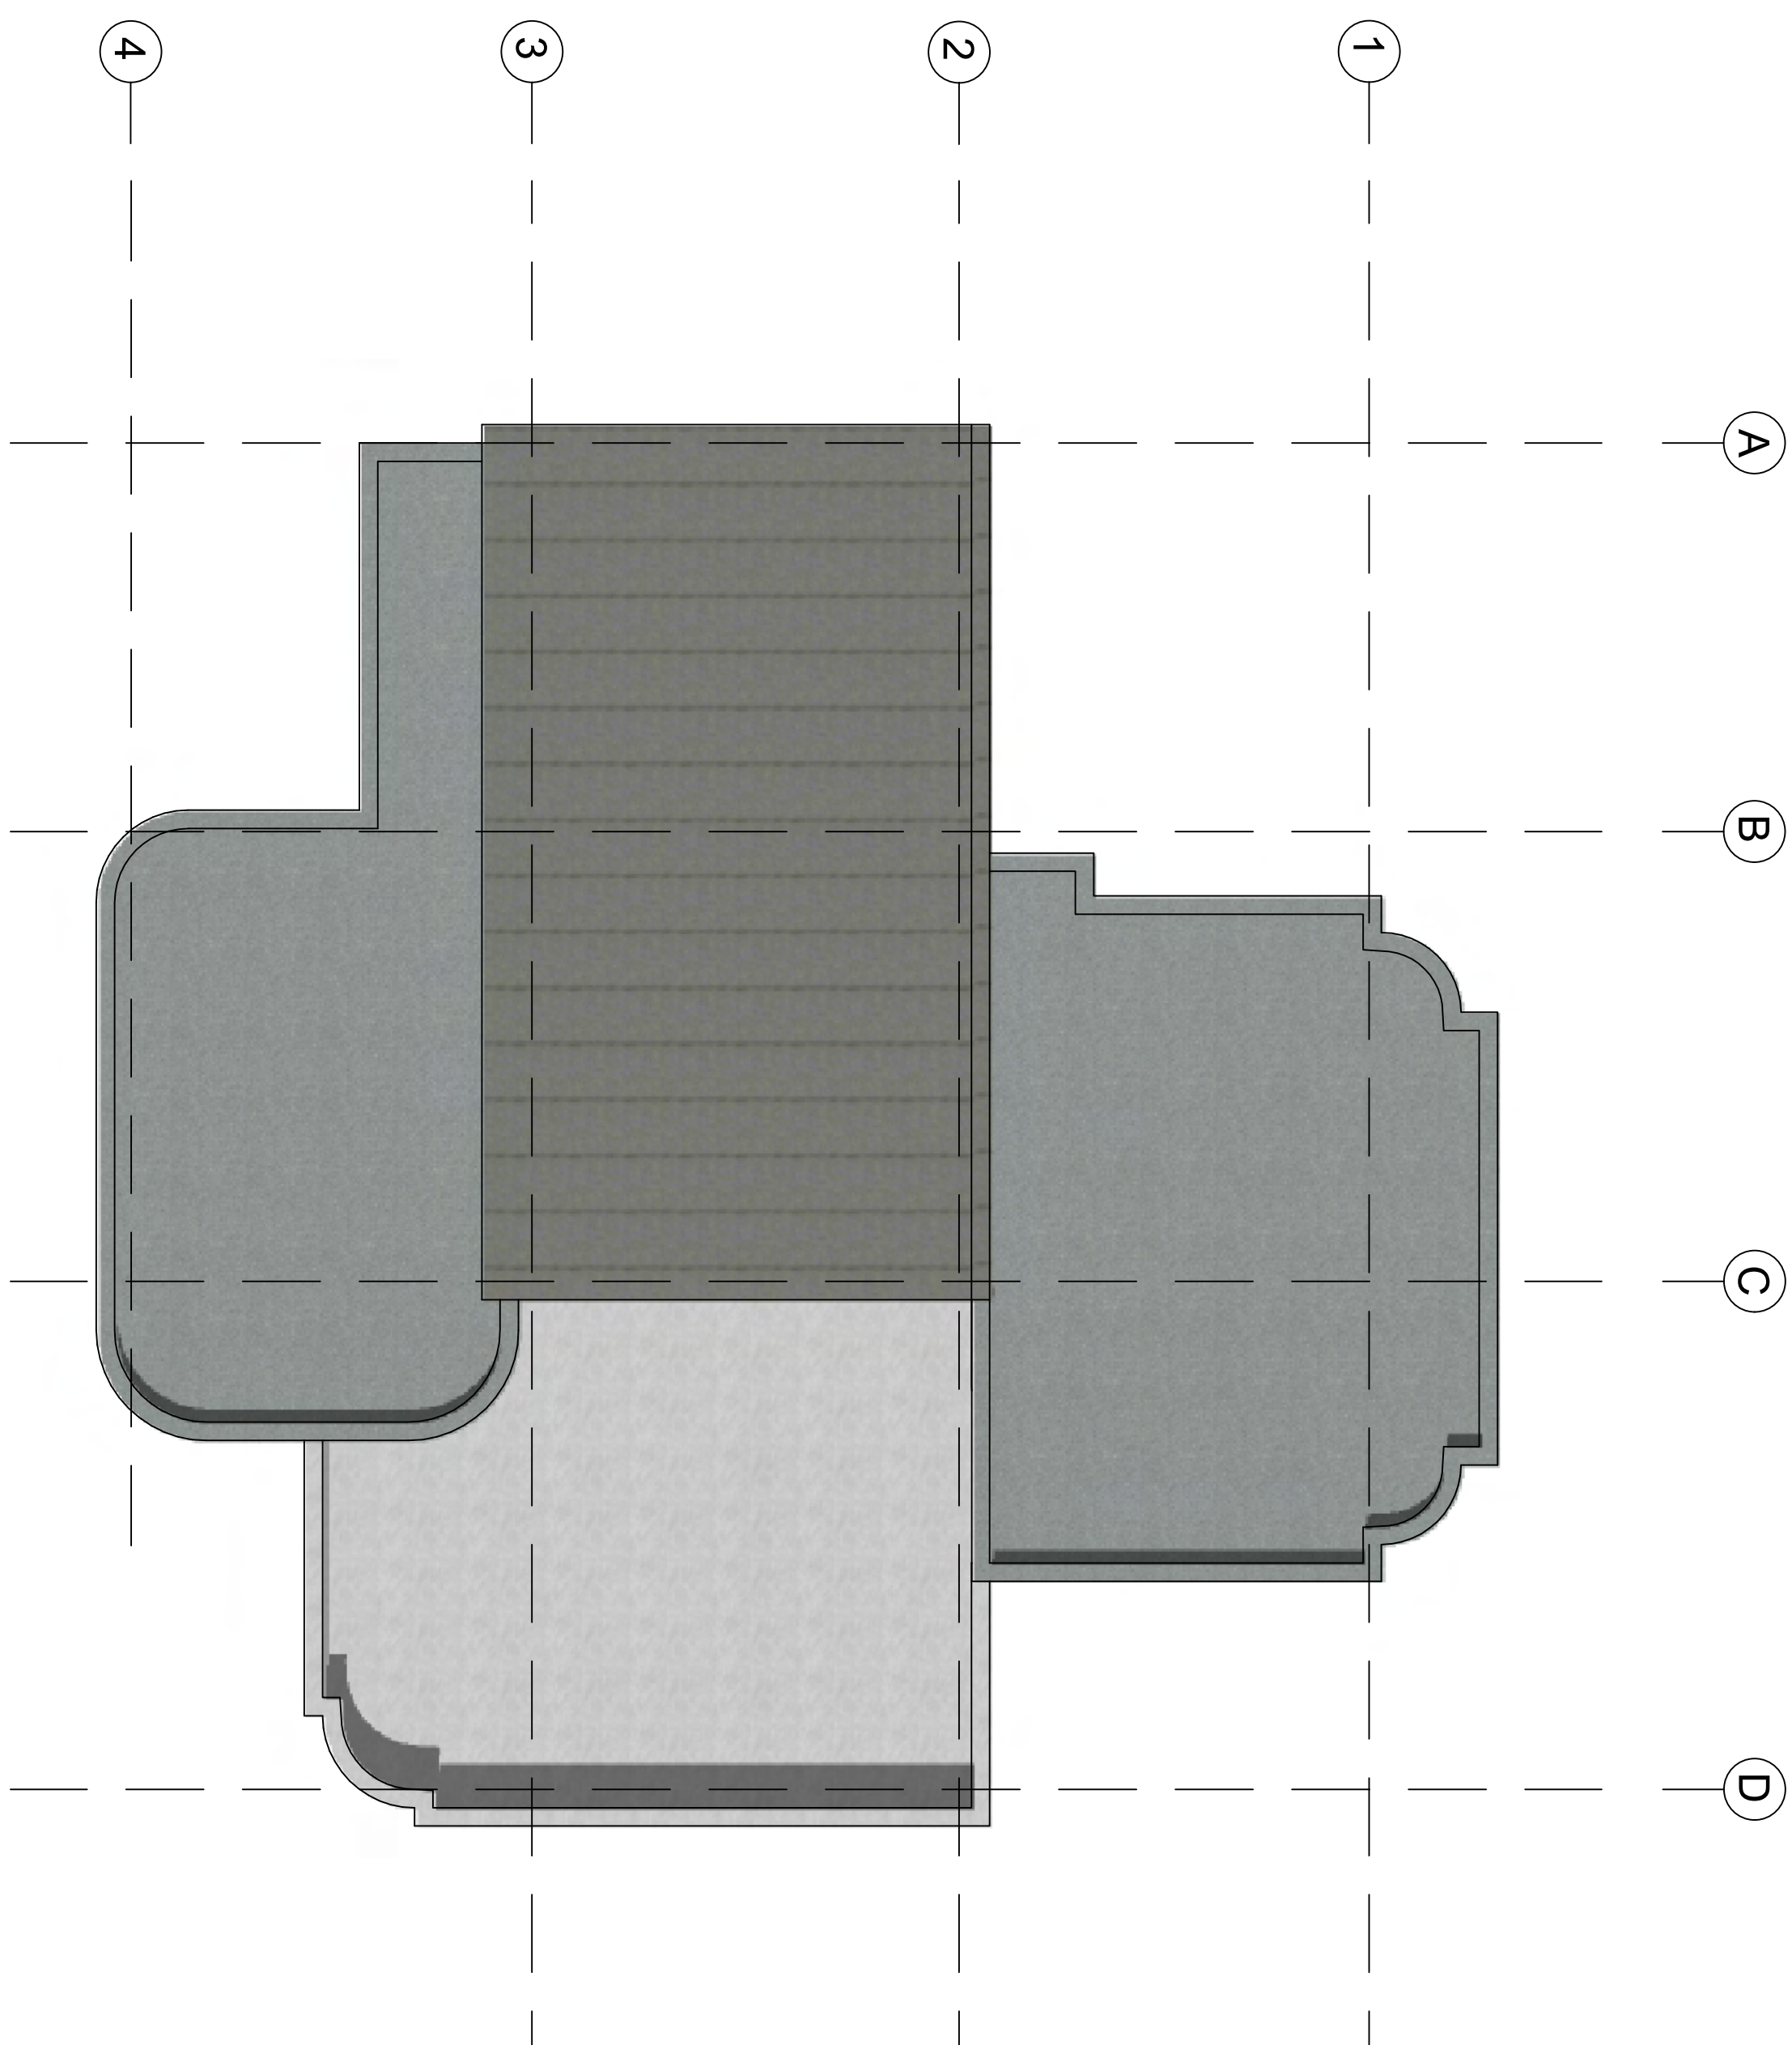

屋頂層平面圖 比例：1/50



西向立面圖 比例：1/50



南向立面圖 比例：1/50



長向剖面圖 A-A 比例：1/50



短向剖面圖 B-B 比例：1/50



北巷立面圖 比例：1/50

